


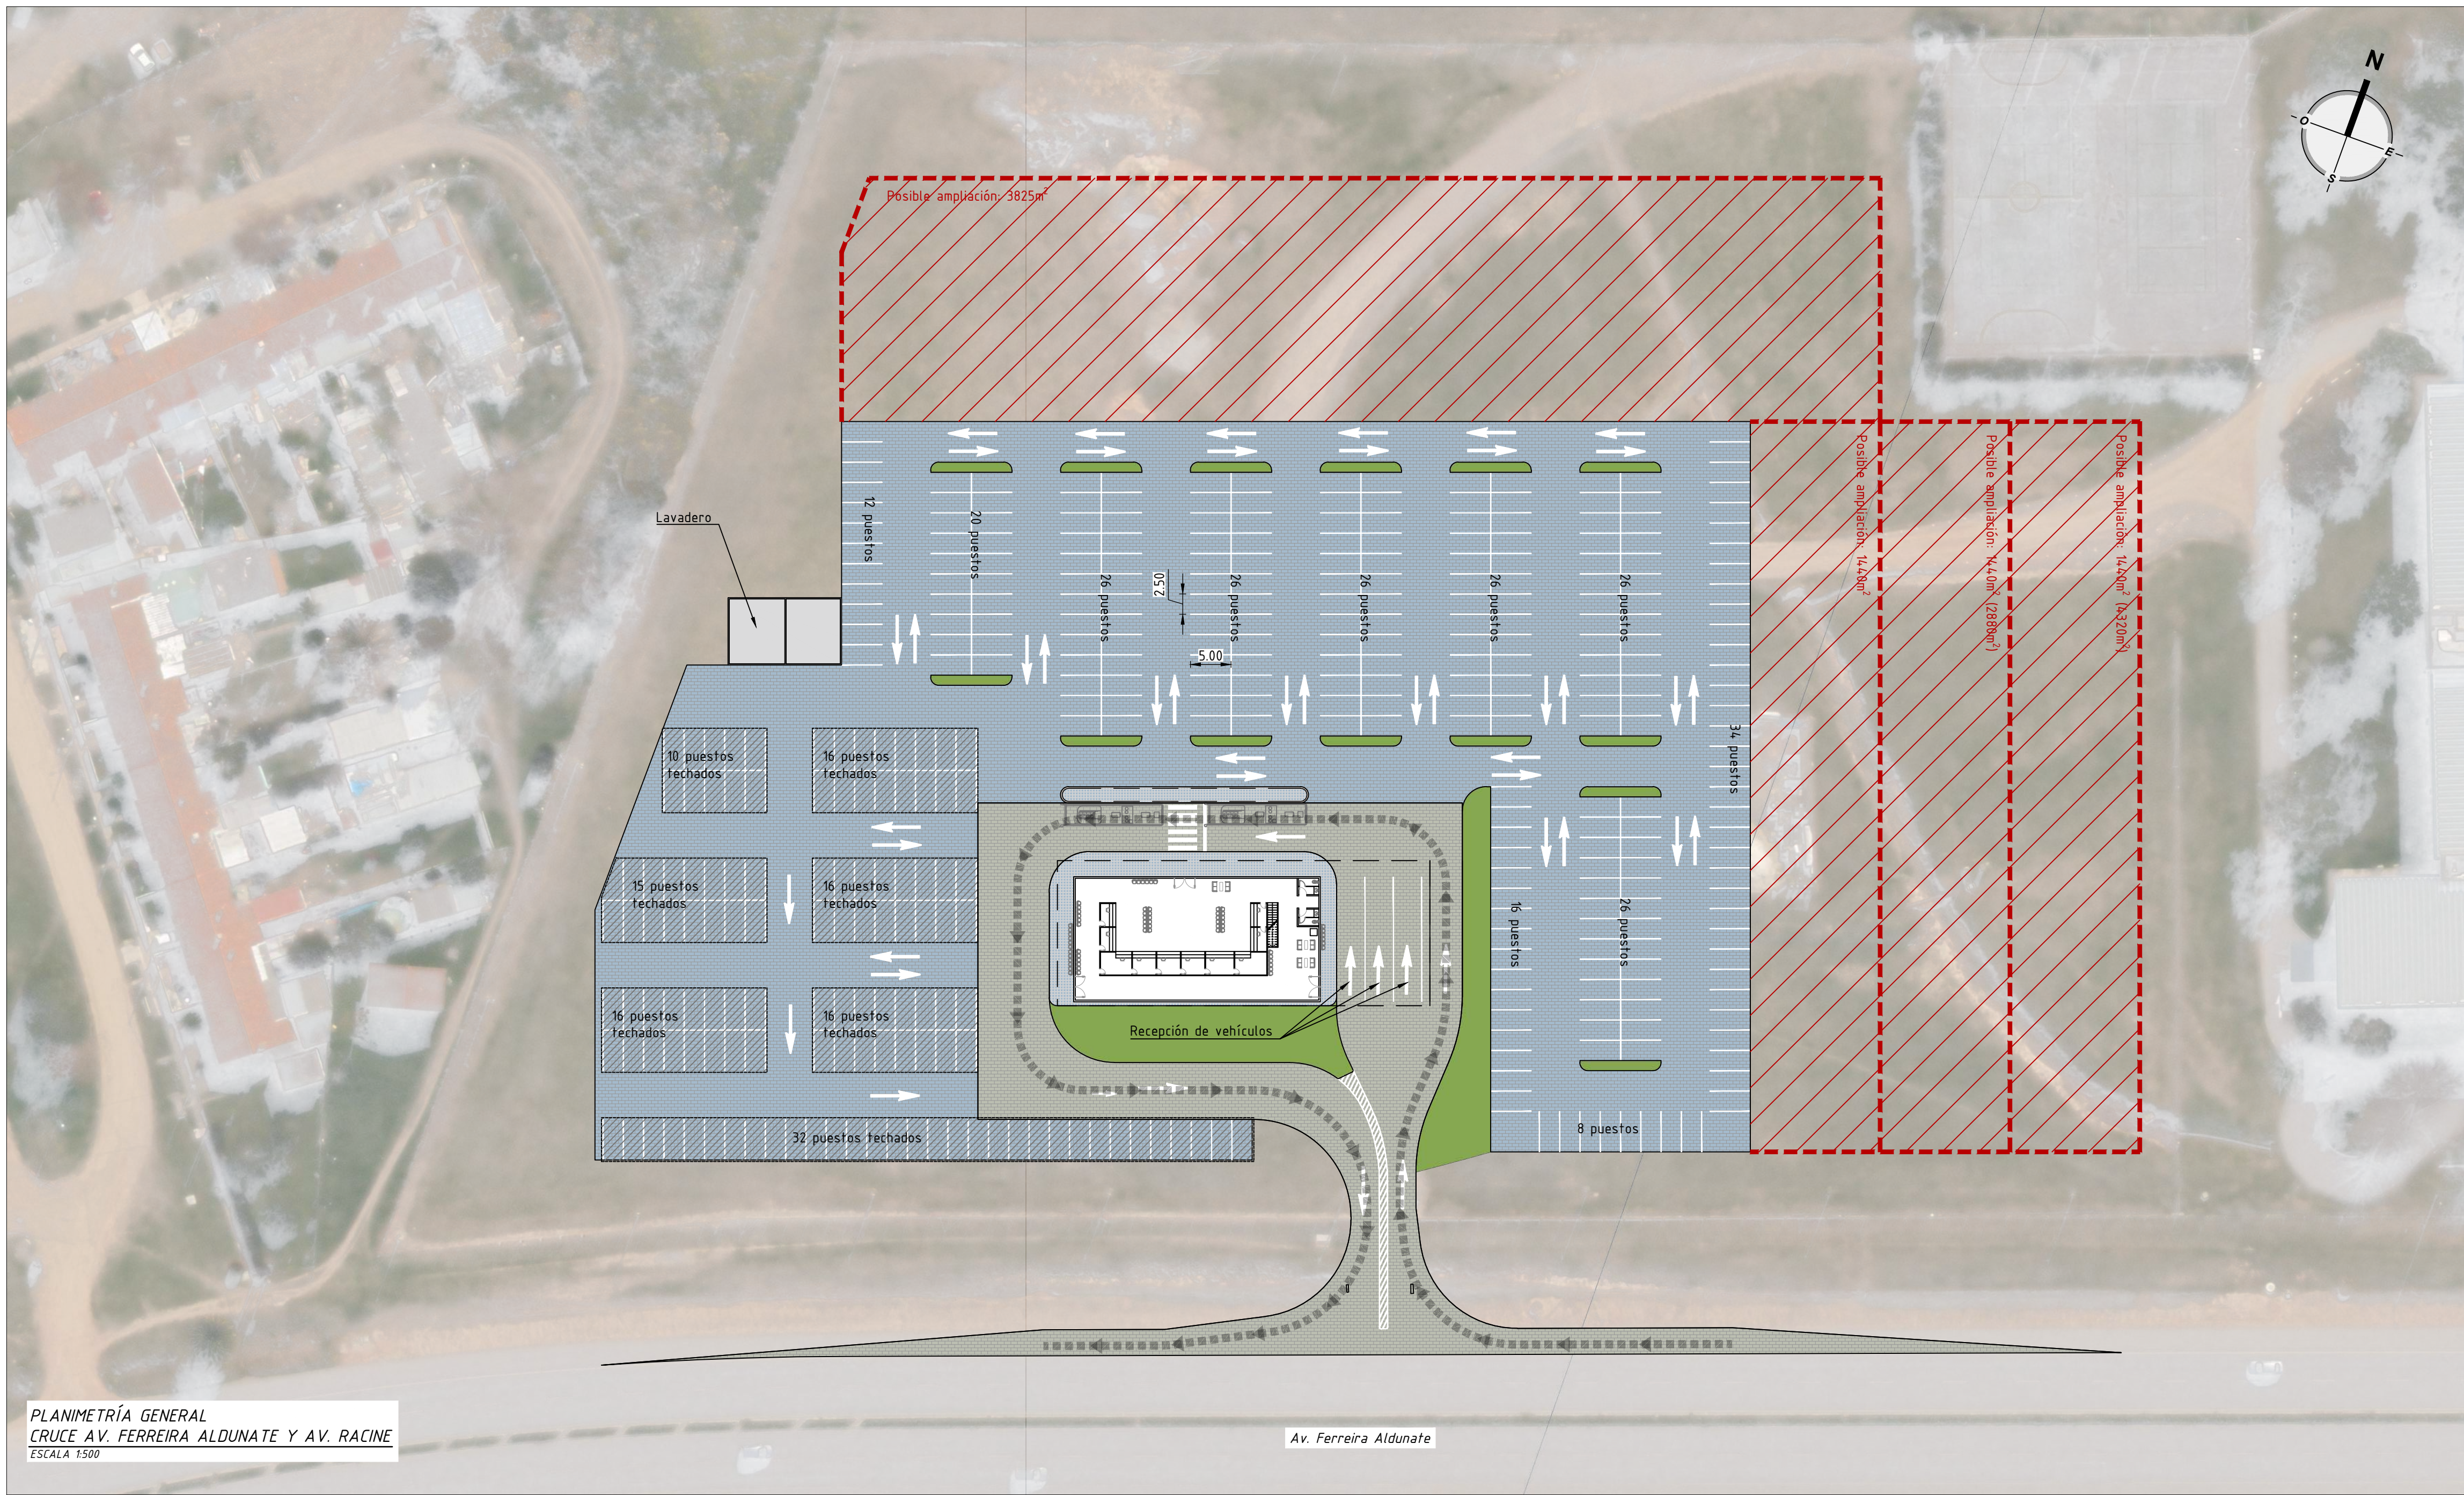


ANTEPROYECTO
NO APTO PARA CONSTRUCCIÓN

REFERENCIAS

SÍMBOLO	DENOMINACIÓN
	Pavimento de adoquines apto para ómnibus
	Pavimento de adoquines para autos
	Posibles ampliaciones
	Recorrido de shuttle

NOTAS:

Área de pavimento para ómnibus: 2150 m²
Área de pavimento para autos: 9000m²
Capacidad total de estacionamiento:
- 121 puestos techados
- 246 puestos abiertos
Dimensiones de puestos: 5.0 m x 2.5 m

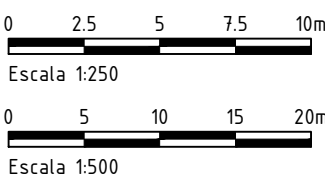

LA IMPRESIÓN DE ESTE DIBUJO EN TAMAÑO DE PAPEL ALTERNATIVO AFECTARÁ SU ESCALA

En proceso

Rev.	Fecha	Proy.	Aprob.	Cambios
HISTORIAL DE GESTIÓN DE CAMBIOS				

				N° PROYECTO: 26.080
CLIENTE: Aeropuertos del Uruguay		TIPO DOCUMENTO: Lámina		ESCALA: 1:500/1:250
PROYECTO: Rentadoras de Autos Aeropuerto de Carrasco		UBICACIÓN: Canelones		HOJA: 1/1
ETAPA: Anteproyecto		PROYECTISTA: Ing. Agustín Ciganda		FECHA: 13-07-2026
DISCIPLINA: Vialidad		TÉCNICO RESPONSABLE: Ing. Martín Ferreira		REVISIÓN: 0a
TIPO: Planimetría General		NÚMERO DE LÁMINA: RAC-AP-VI-PG-01		